

opdrachtgever:

Woningstichting Sint Joseph

programma:

7 starterswoningen

start:

opdracht


7 starterswoningen op geluidsbelaste locatie

2004


kuiperstraat

realisatie:

2005

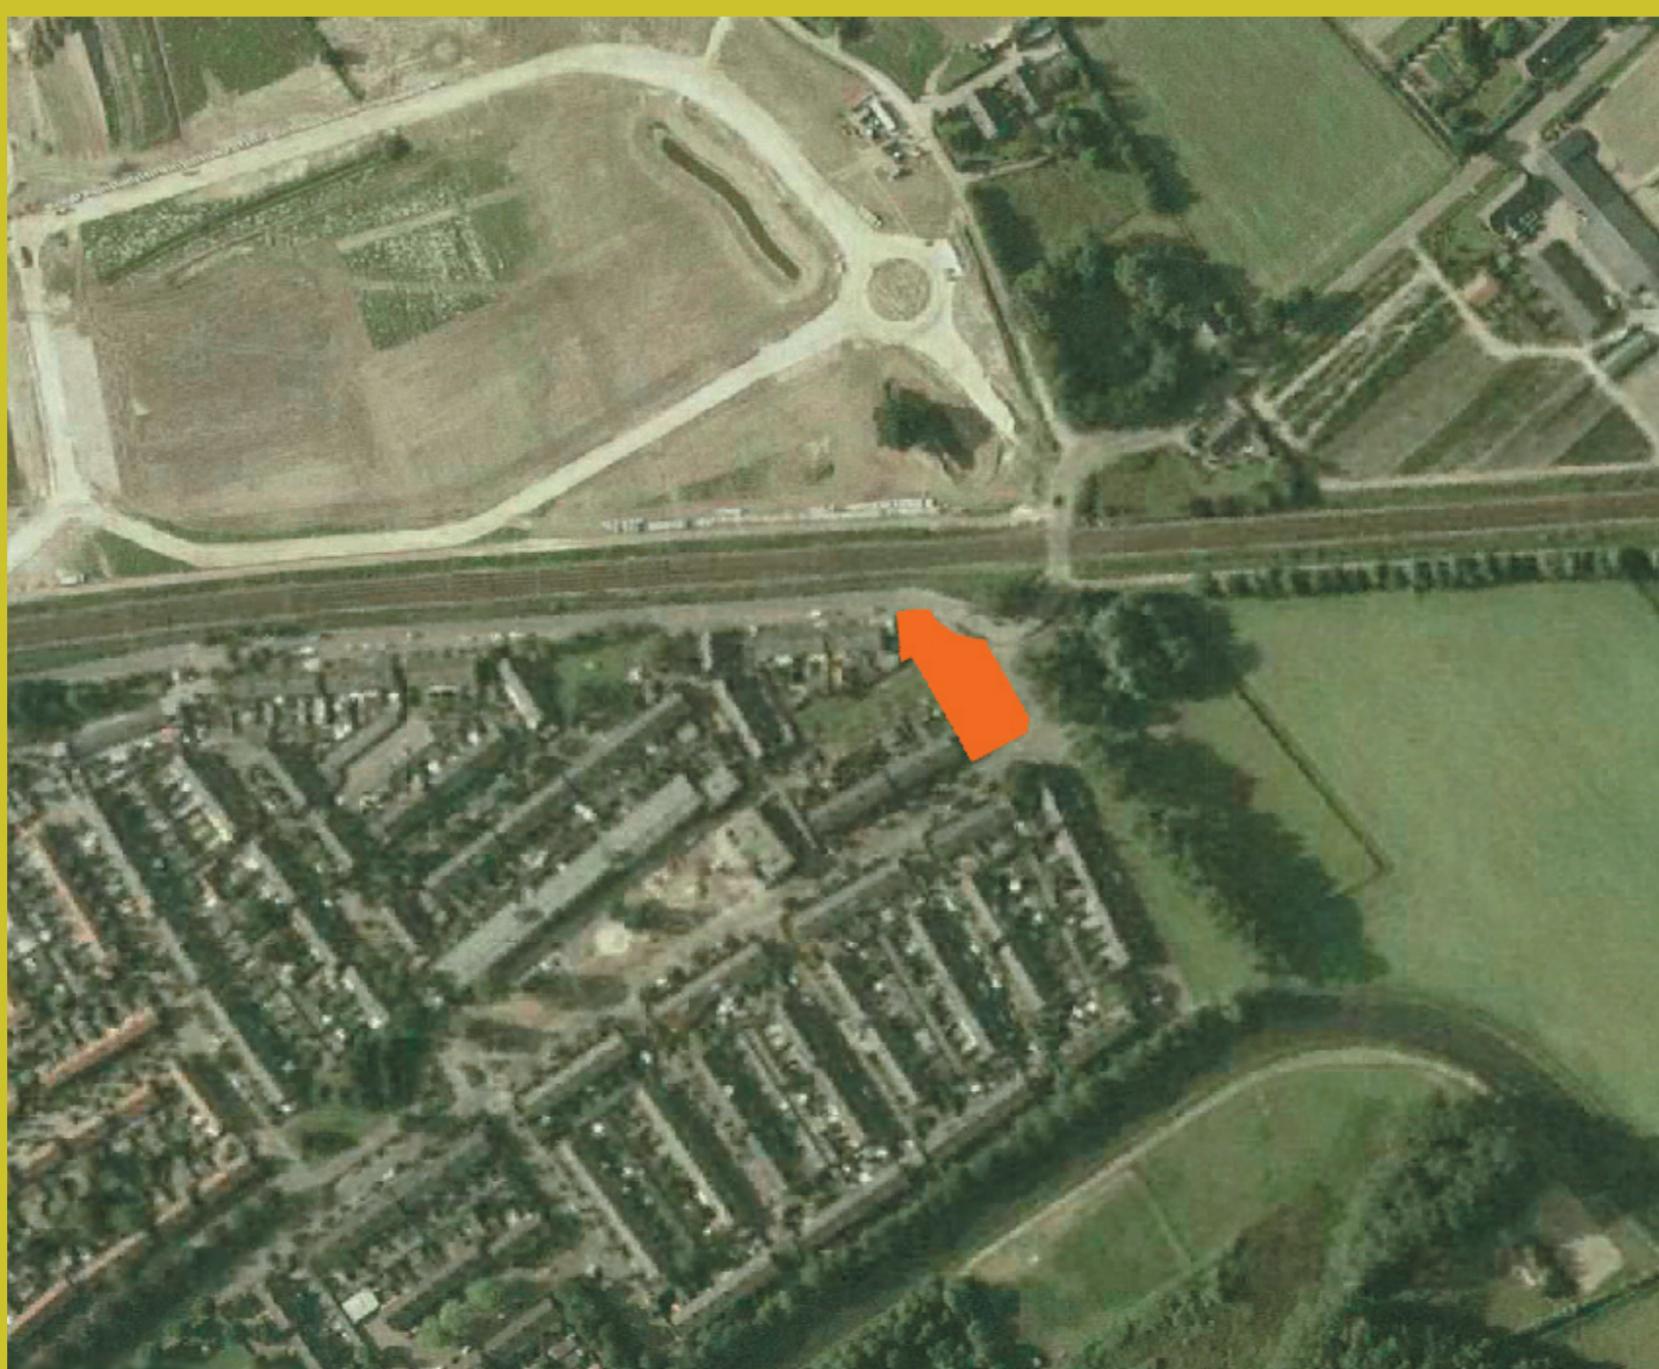

oisterwijk

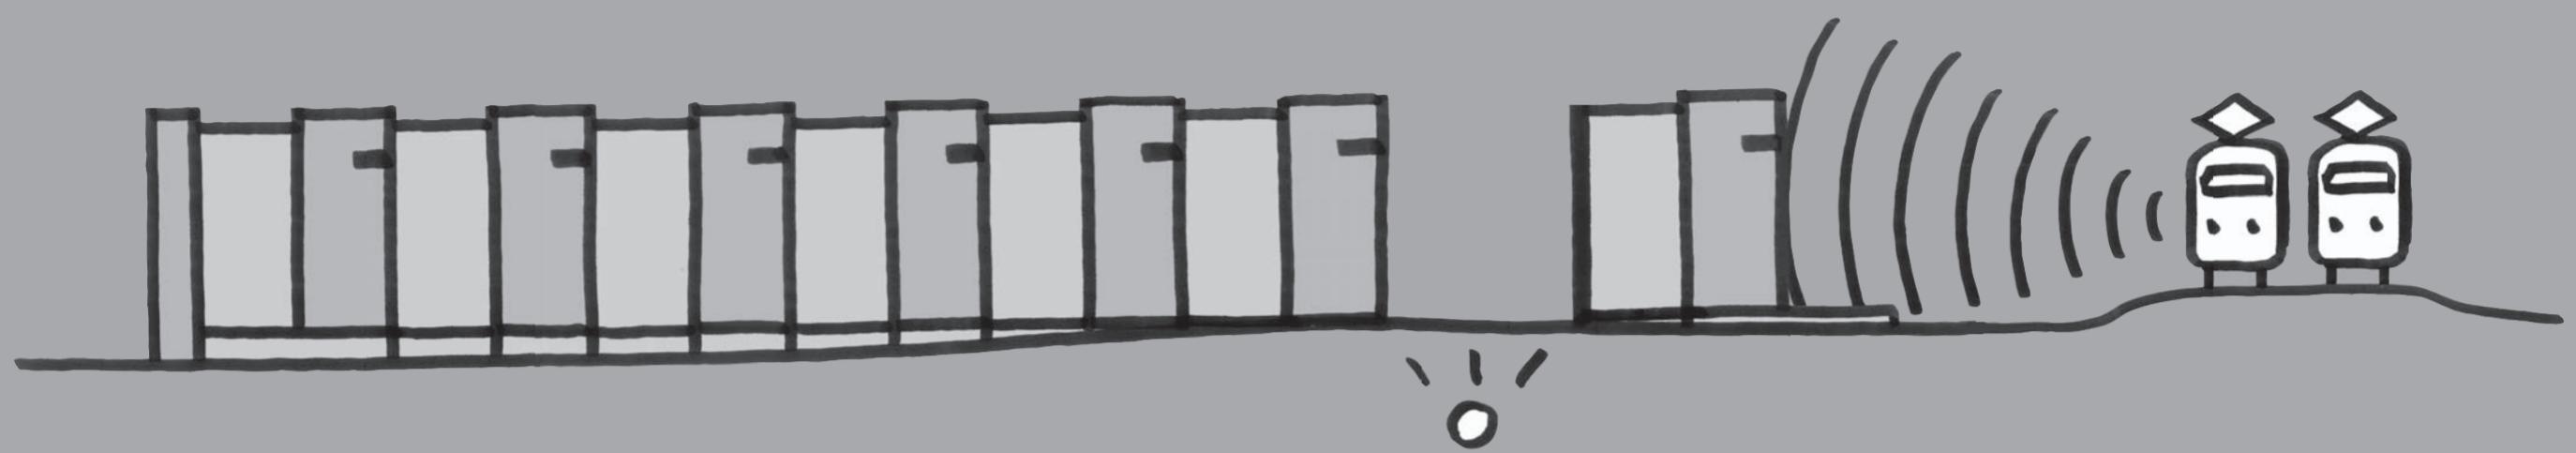


uitdagingen

# kuiperstraat


oisterwijk

geluid:

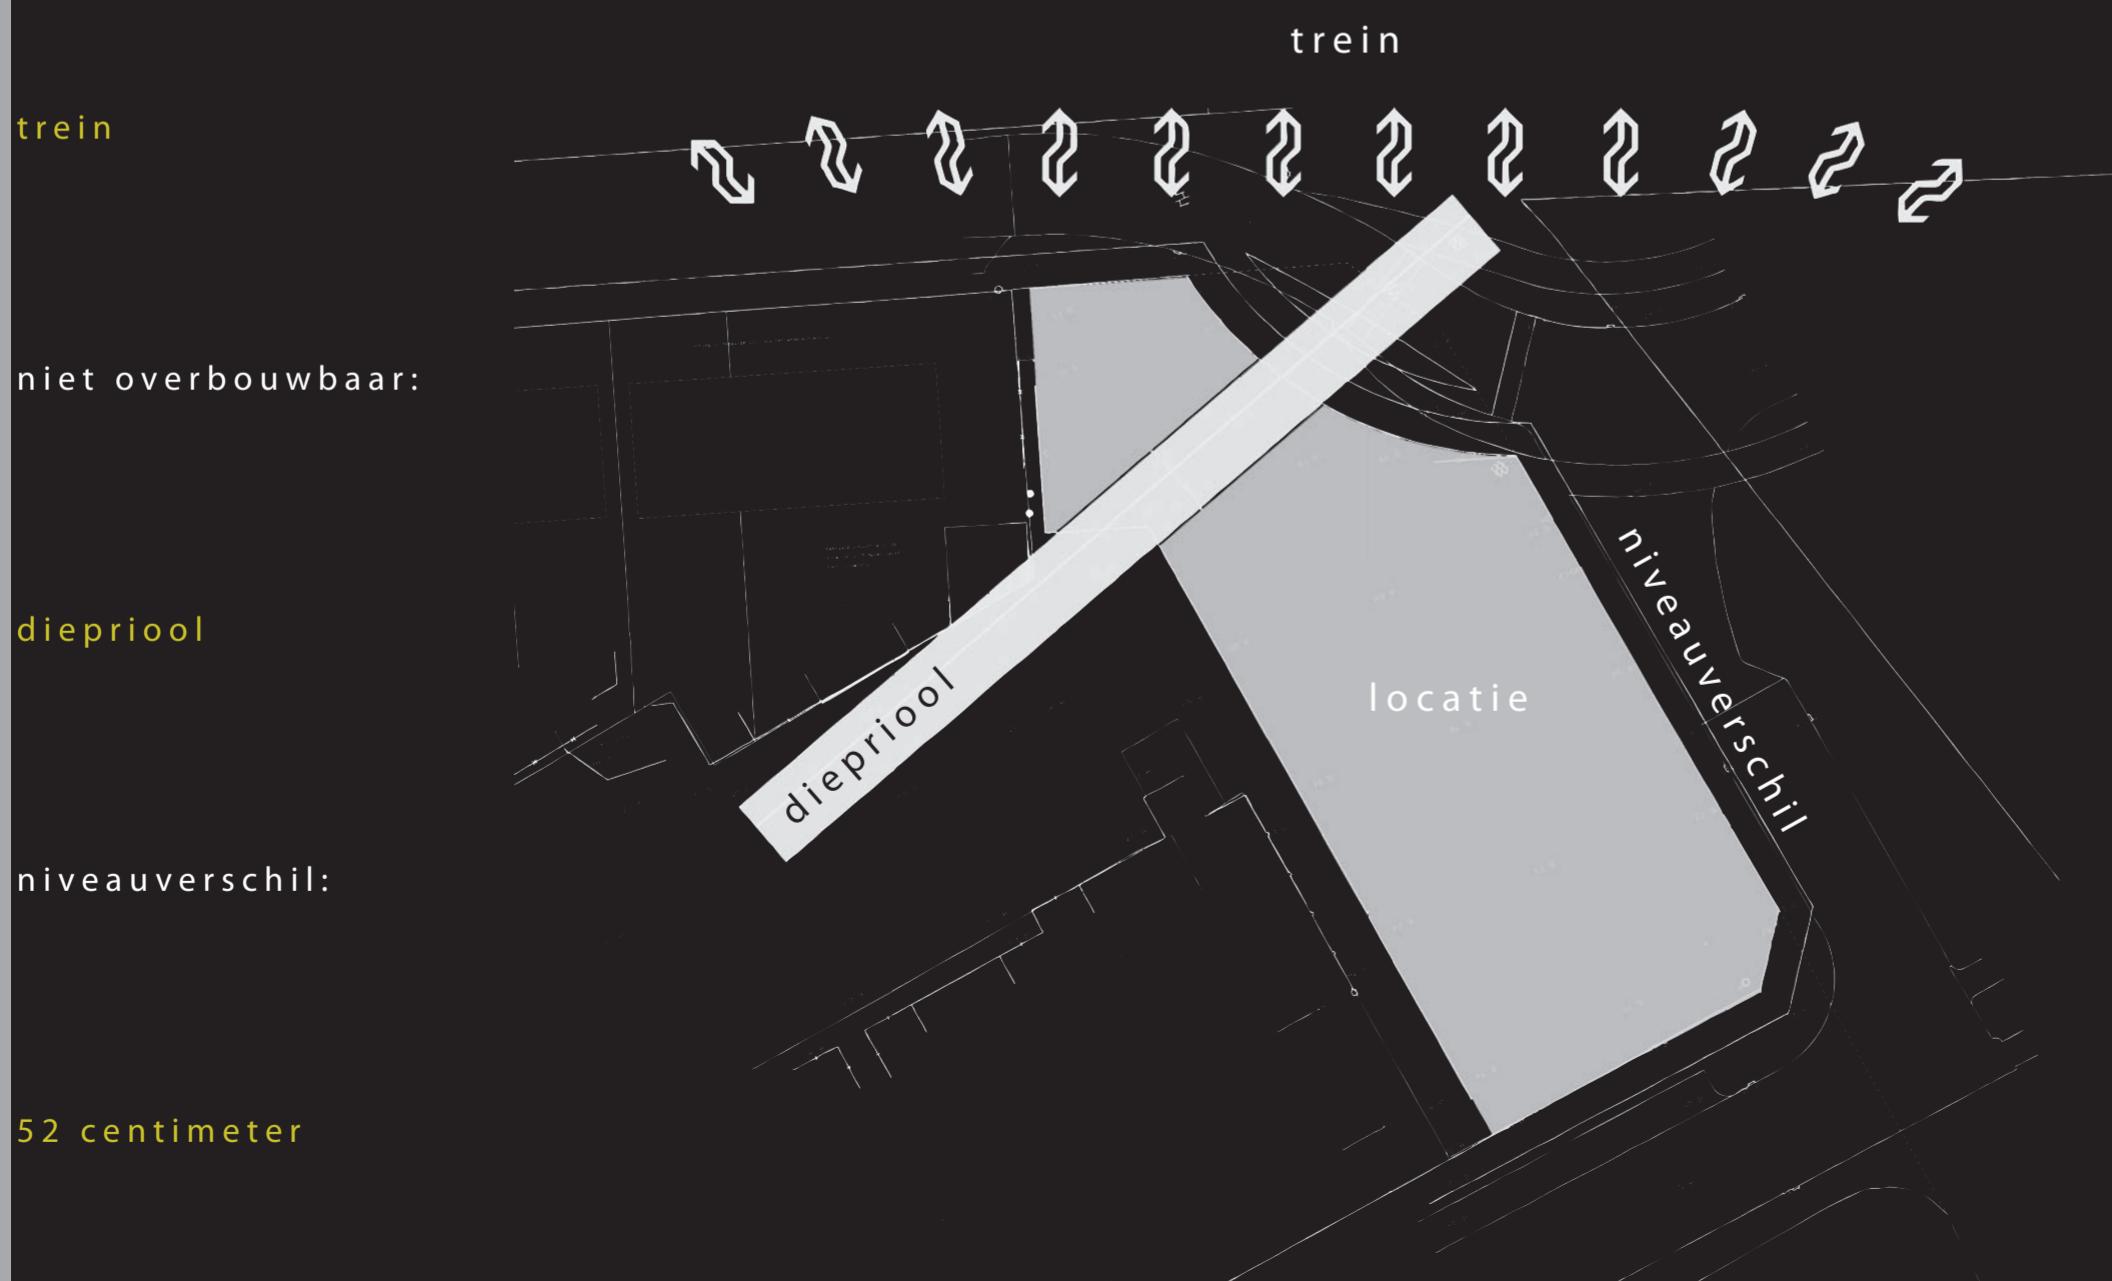

plattegrond

TERBURGHTEWEG

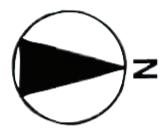

1 2 5 10M

KUIPERSTRAAT


kunstwerk

NICOLAAS VAN  
ESCHSTRAAT


totaalplan

# kuiperstraat


voorgevel west

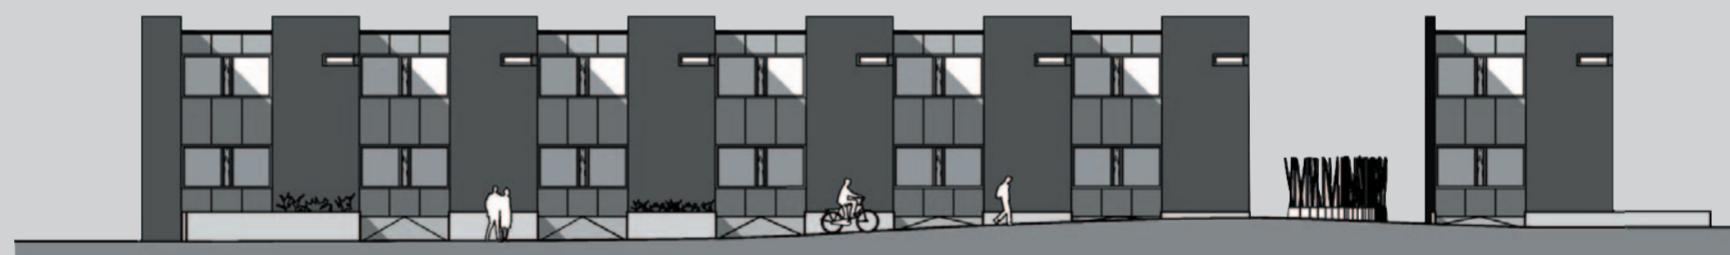

achtergevel oost


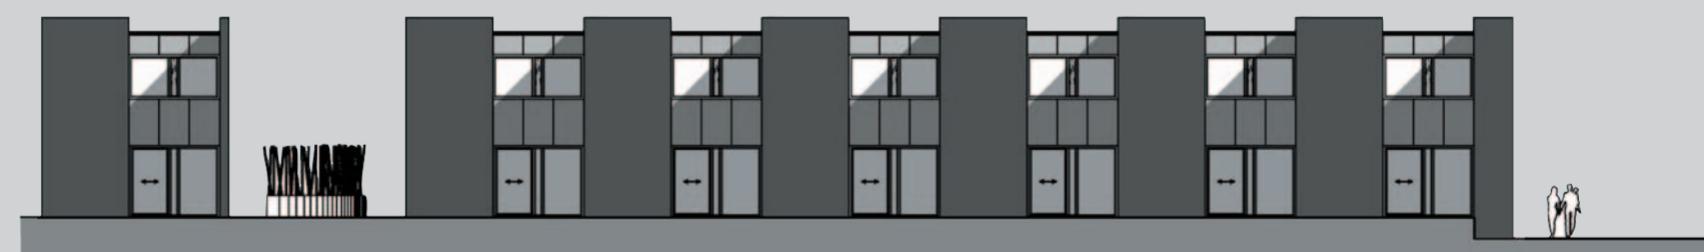


zijgevel noord

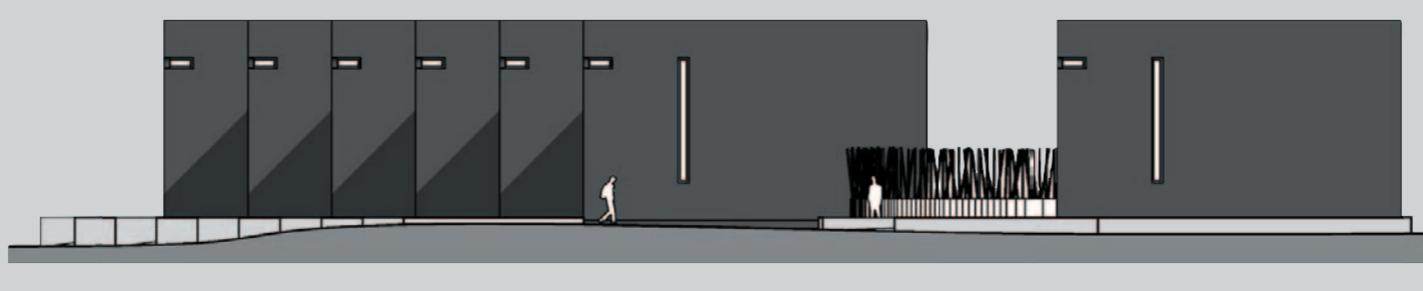


oisterwijk

1 2 5 10M

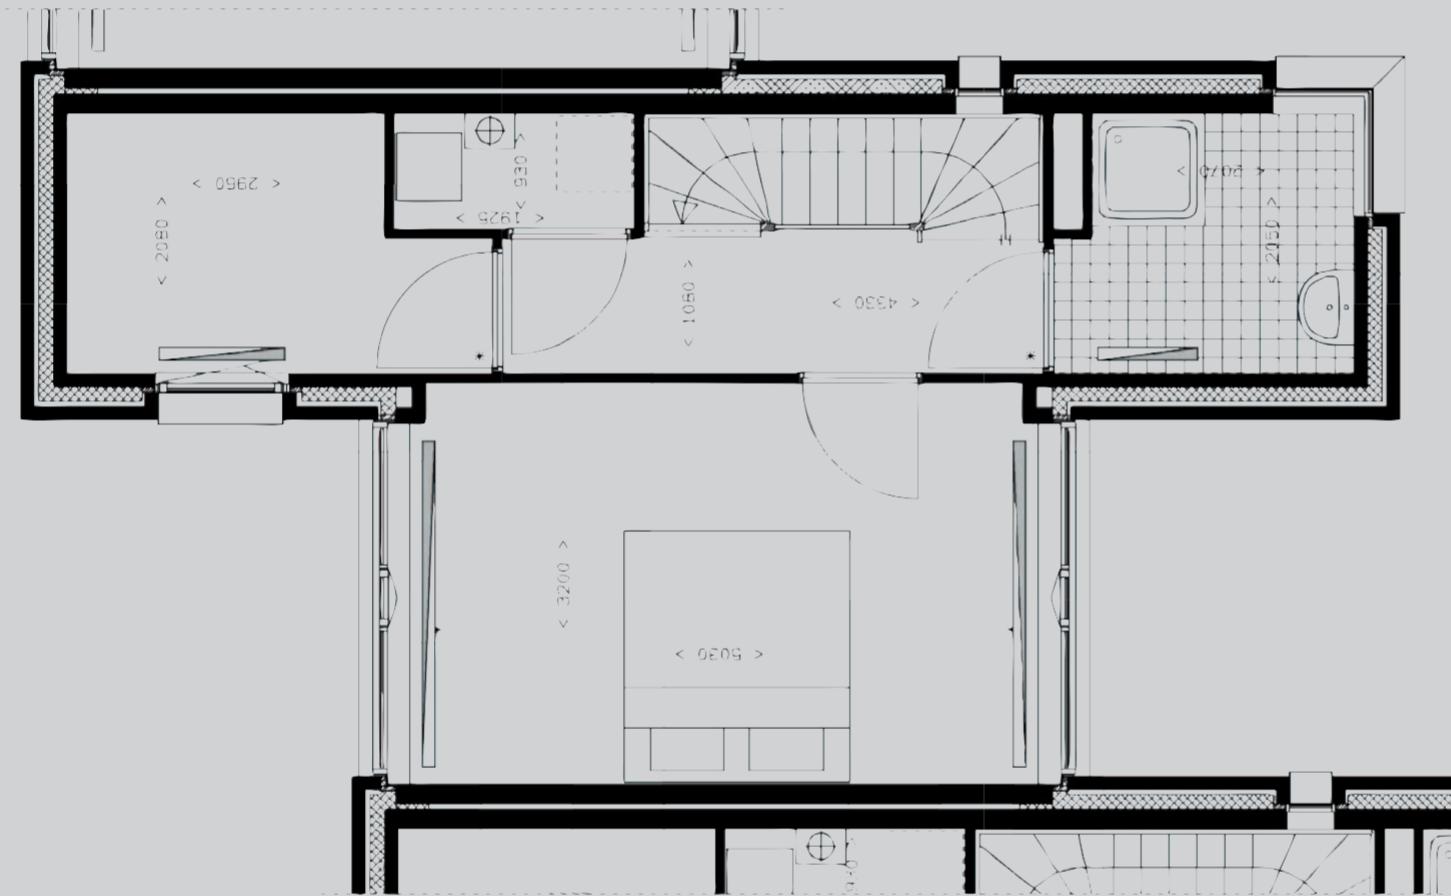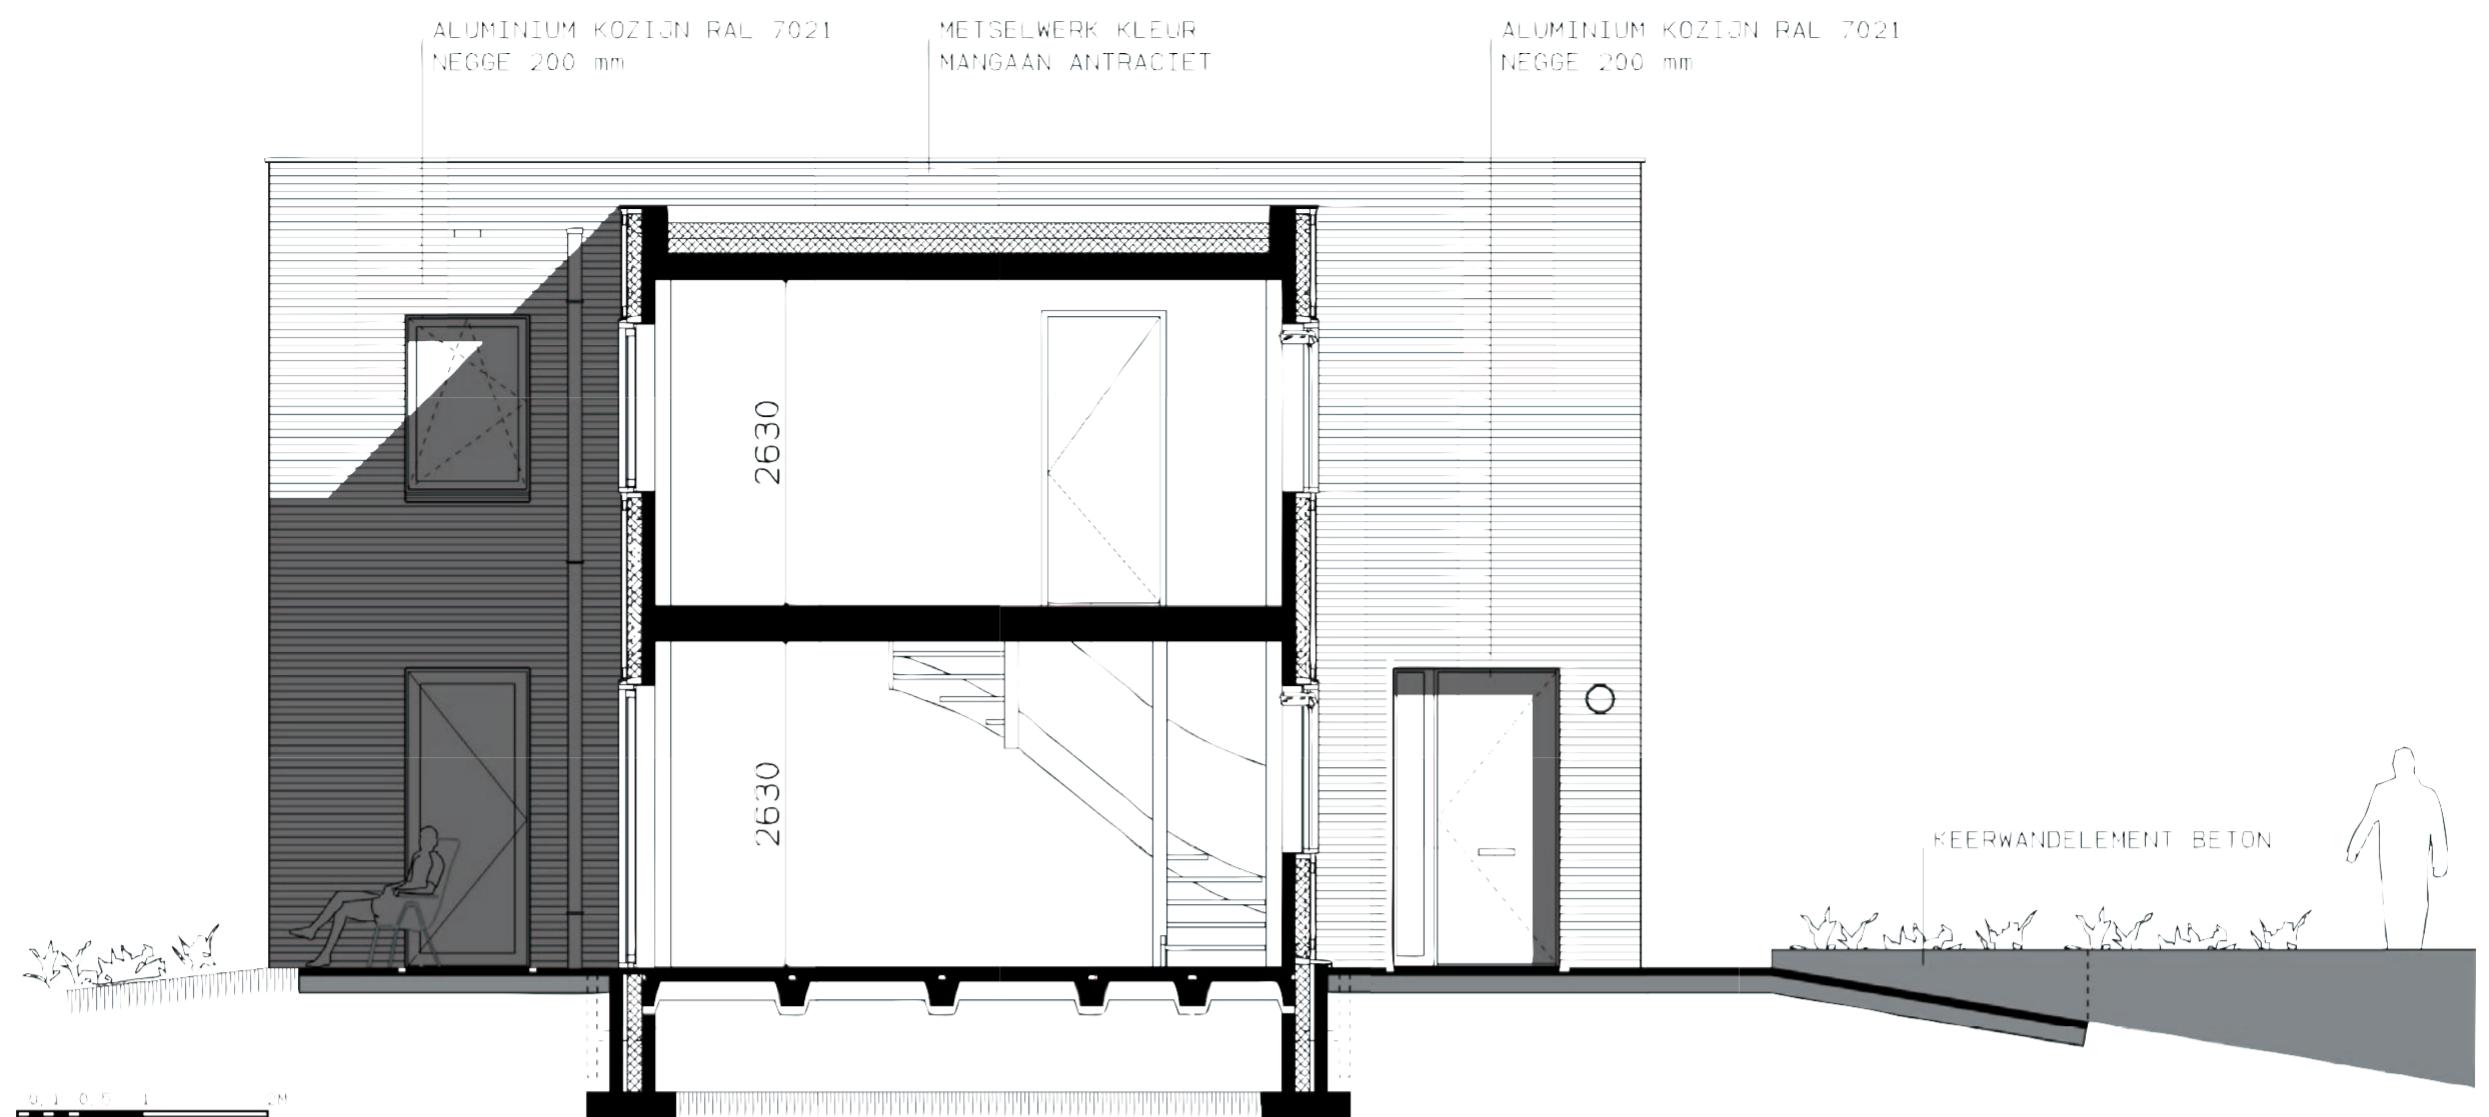

1e verdieping

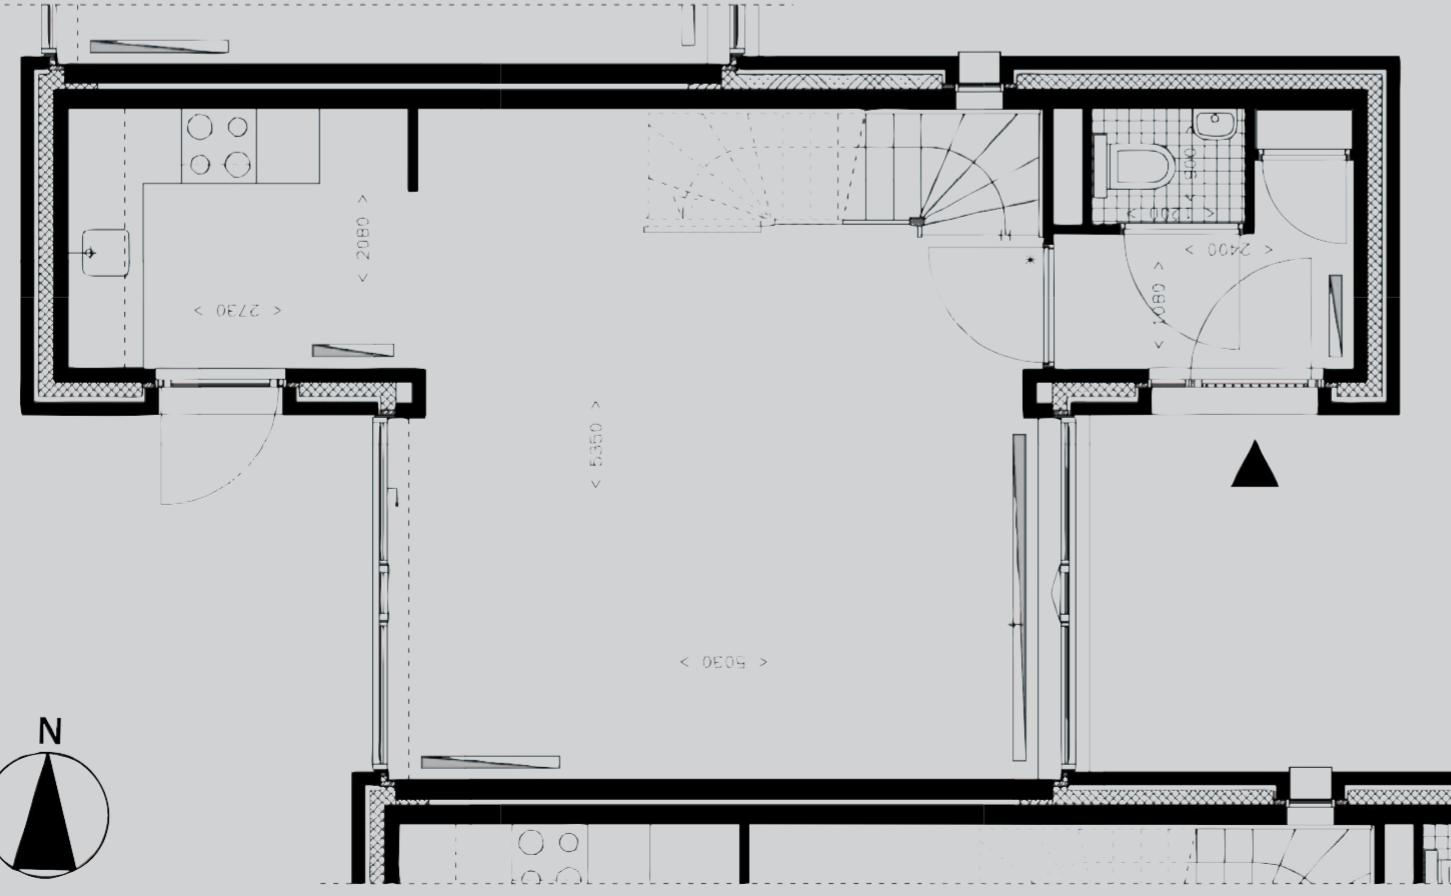

begane grond



# kuiperstraat

oosterwijk


ALUMINIUM KOZIJN RAL 7021

ALUMINIUM KOZIJN RAL 7001

COLORBEL F 238 HM  
GERIBBELO GLAS  
KLEUR LICHTGRIJS  
BLIND BEVESTIGD

ALUMINIUM DAKTRIM

METSELWERK KLEUR  
MANGAAN ANTRACIET

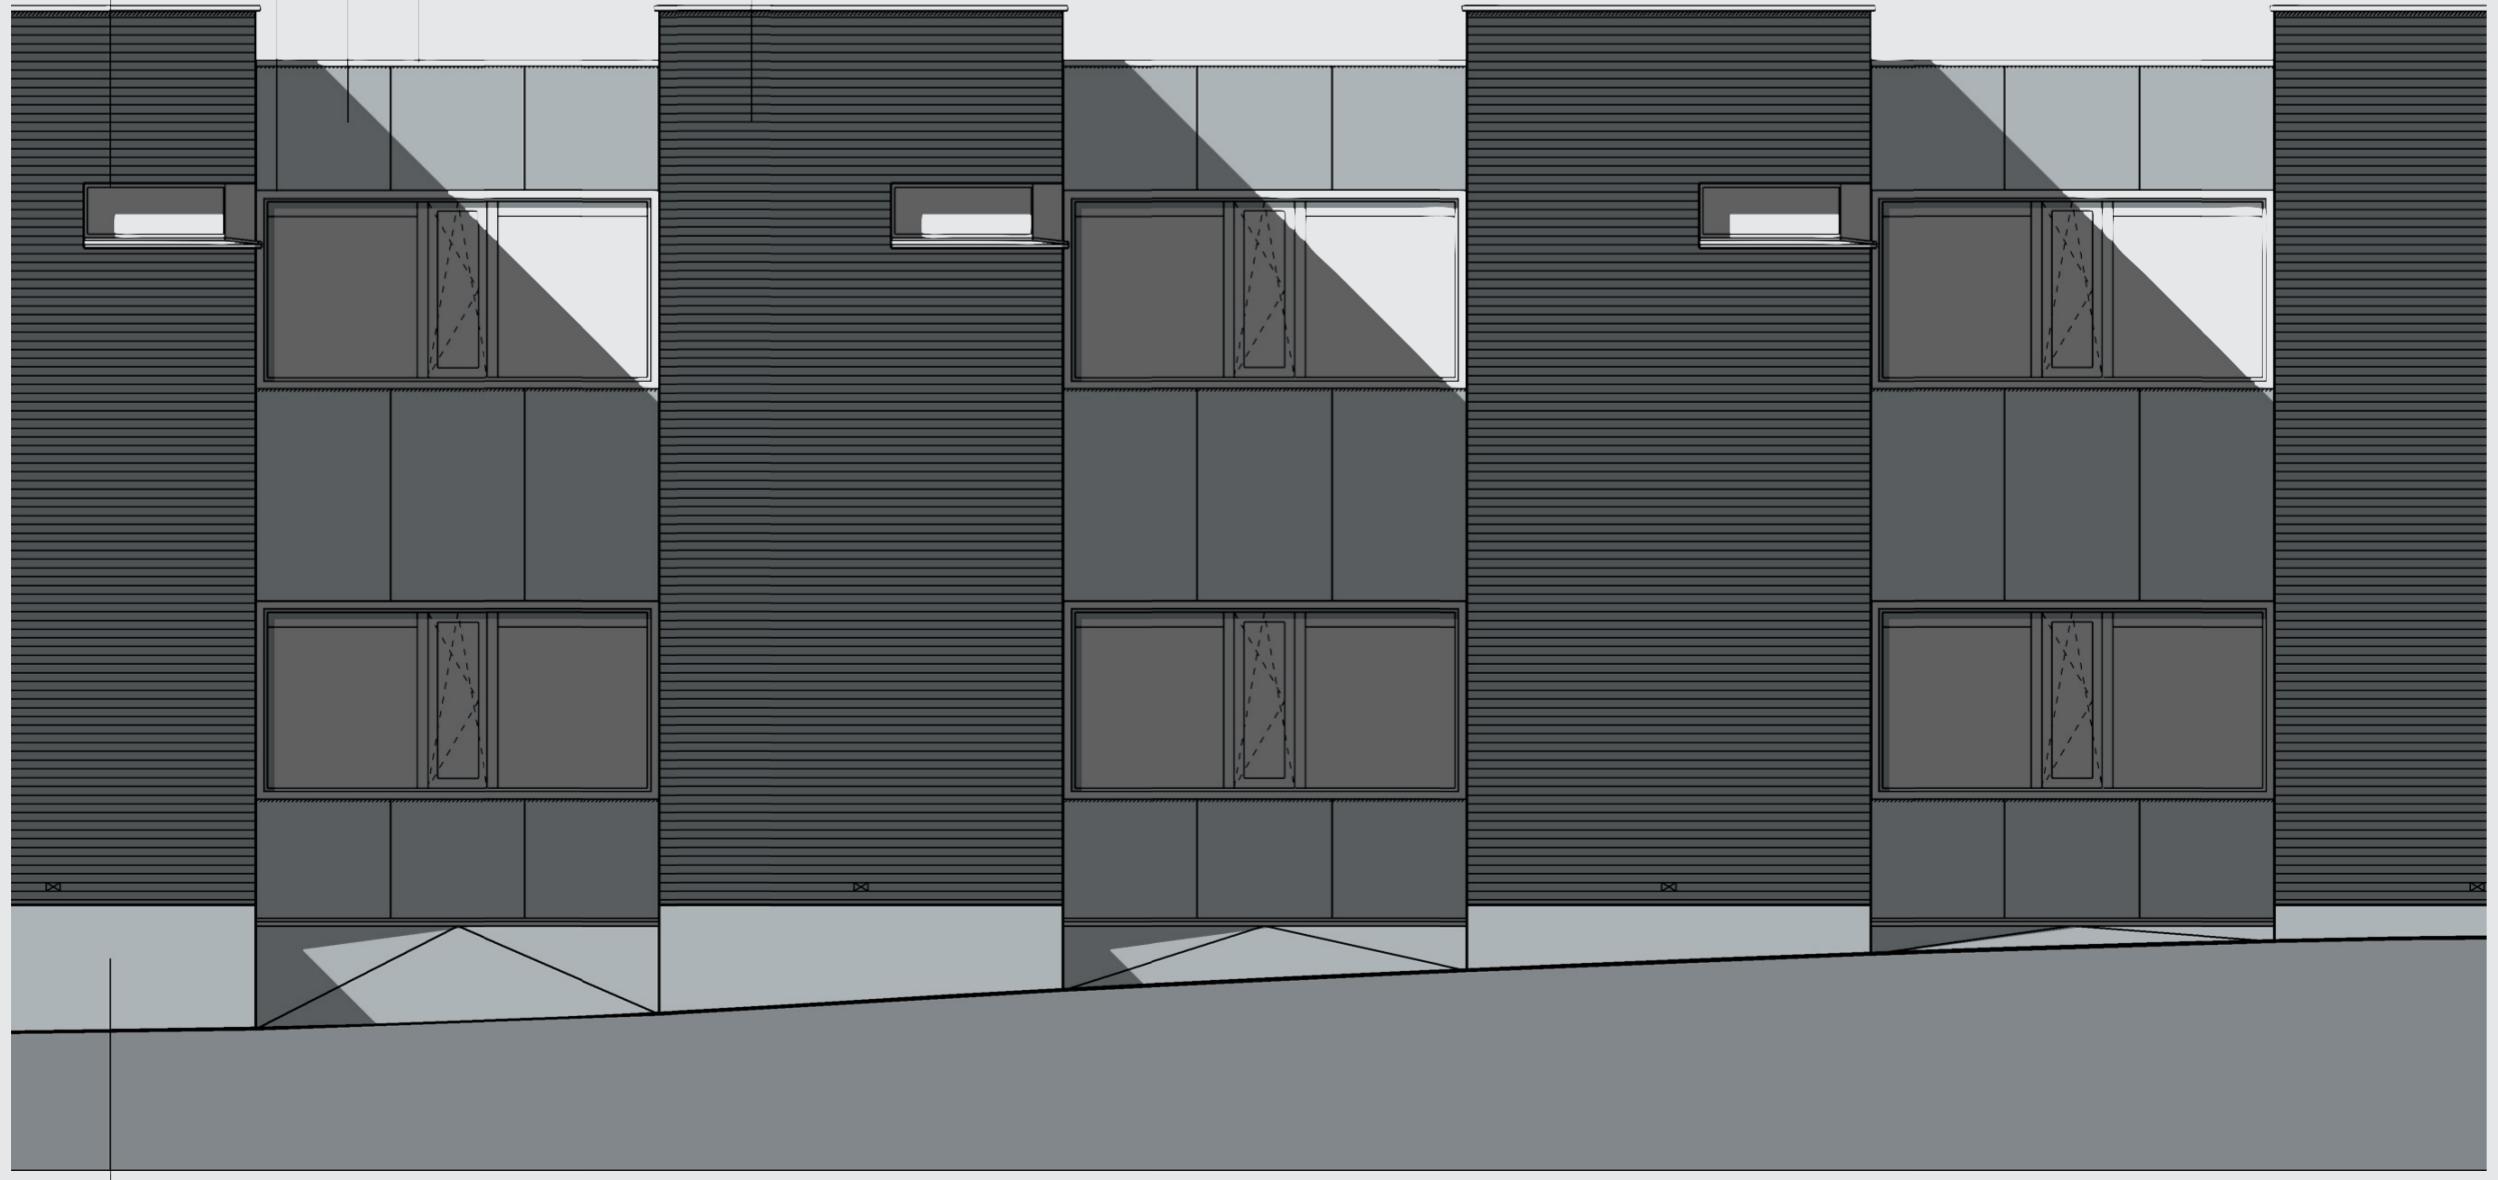

KEERWANDELEMENT BETON



Aan het spoortraject Tilburg-Eindhoven komen zeven starterswoningen op een beeldbepalende locatie aan de rand van Oisterwijk. De woningen markeren de oostentree van het dorp en samen vormen zij een wand richting het spoortraject. Door de woningen ten opzichte van elkaar te verschuiven ontstaan er geluidsluwe zones aan de voor-en achtergevel en vormen de woningen tegelijkertijd een begrenzing van het open bouwblok.

Volumes van donkere baksteen met diepe negges geven de noord- en zuidgevel een gesloten karakter. Hiertussen staan kleinere volumes met een meer open karakter, bekleed met transparant en diffuus glas in combinatie met opliggende aluminium kozijnen. Het contrast tussen licht en donker, open en gesloten, klein en groot wisselen elkaar af en geven het plan een dynamisch beeld.

Dit wordt nog versterkt door het

aanwezige niveauverschil in de locatie. Door een plint ter plaatse van de voortuinen en een hellingsbaan bij de woningentree te maken, krijgt de overgang tussen privé en openbaar zowel een hard als zacht karakter. Het niet bebouwbare gedeelte ter plaatse van het dieprioel krijgt een nog nader te bepalen invulling in de vorm van een kunstwerk. Samen met de woningen zal dit een bijzondere entree voor Oisterwijk vormen.

## kuiperstraat

oisterwijk